

KEYPLAN

LEGENDES ET NOTES

Le Maître d'ouvrage :

FONDATION ISMAIL OMAR GUELLE

Entreprise



DJI - FU SARL

INTITULE DU PROJET:


PROJET DE CONSTRUCTION
D'UNE POLYCLINIQUE A NASSIB

TITRE DU PLAN

LOT: ARCHITECTURE

PLAN RDC

Dessiné par:	Verifié:
Approuvé:	Revisé:
Echelle ● A1	DWG. No. A-01
DATE: 26/04/2026	

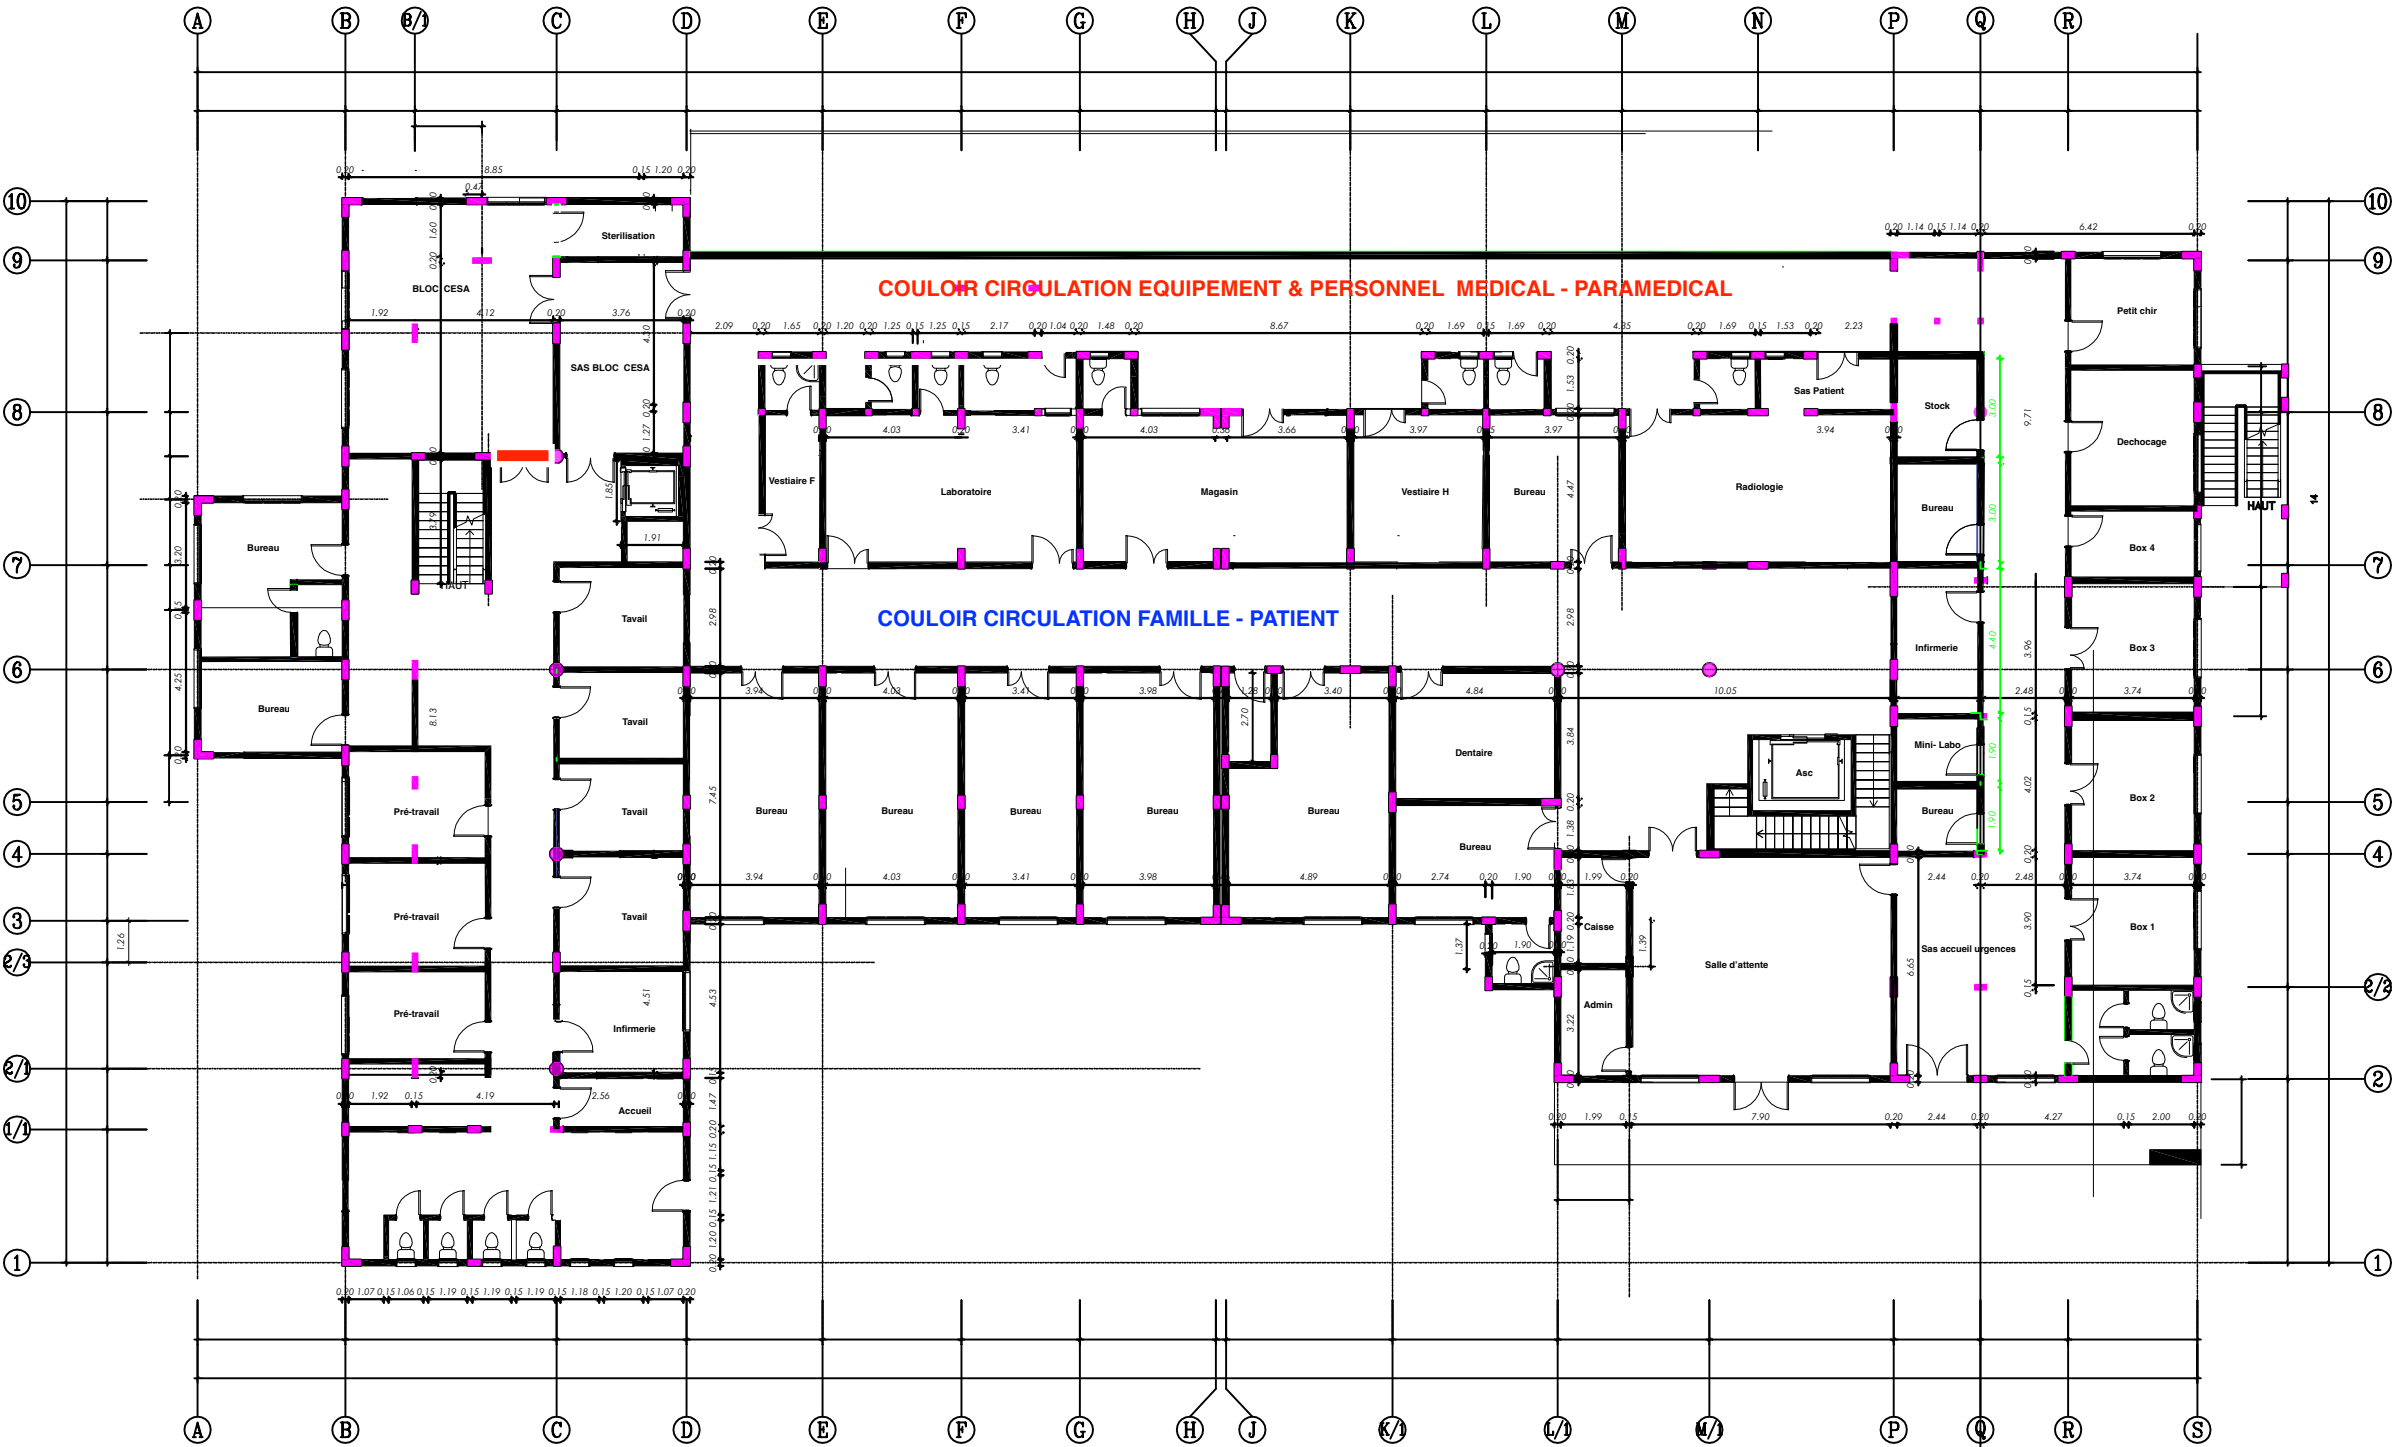

PLAN RDC